FRAME AND OVERALL SIZE

For the welder - all dimensions shown here are provisional until site measurements are confirmed

FRONT VIEW

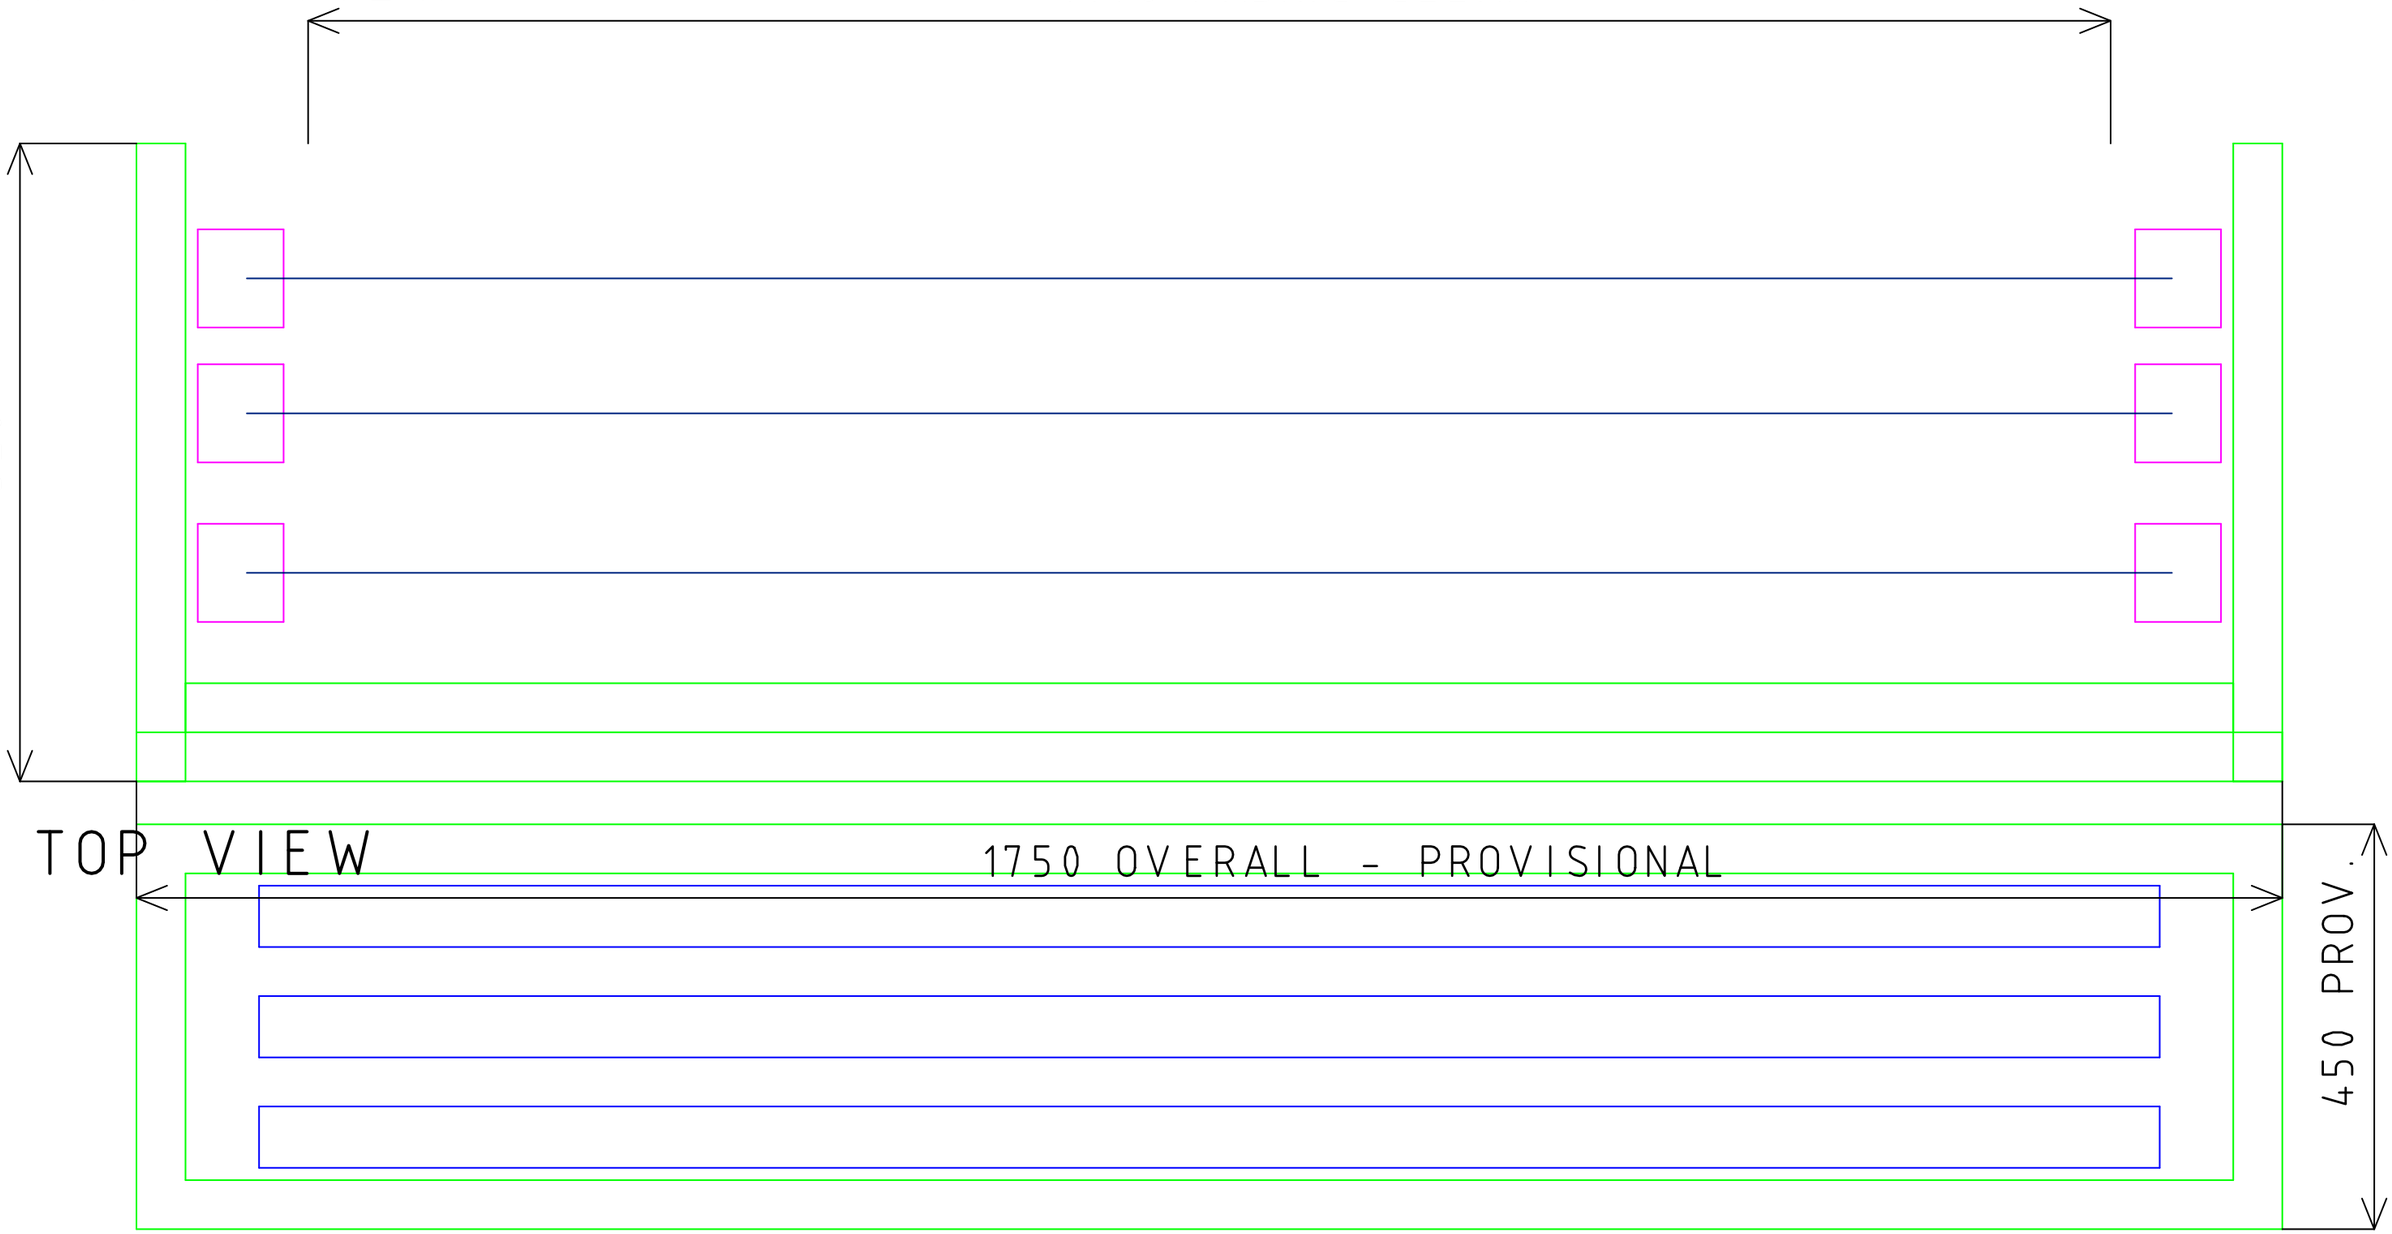

TOP VIEW

FRAME: 40 x 40 x 2 mm MS SHS | 4 mm FILLET WELDS | ADD FEET AND GUARDS

	FABRIC METER S2 / 4	REV C A3 1:5	PROVISIONAL VERIFY FIRST